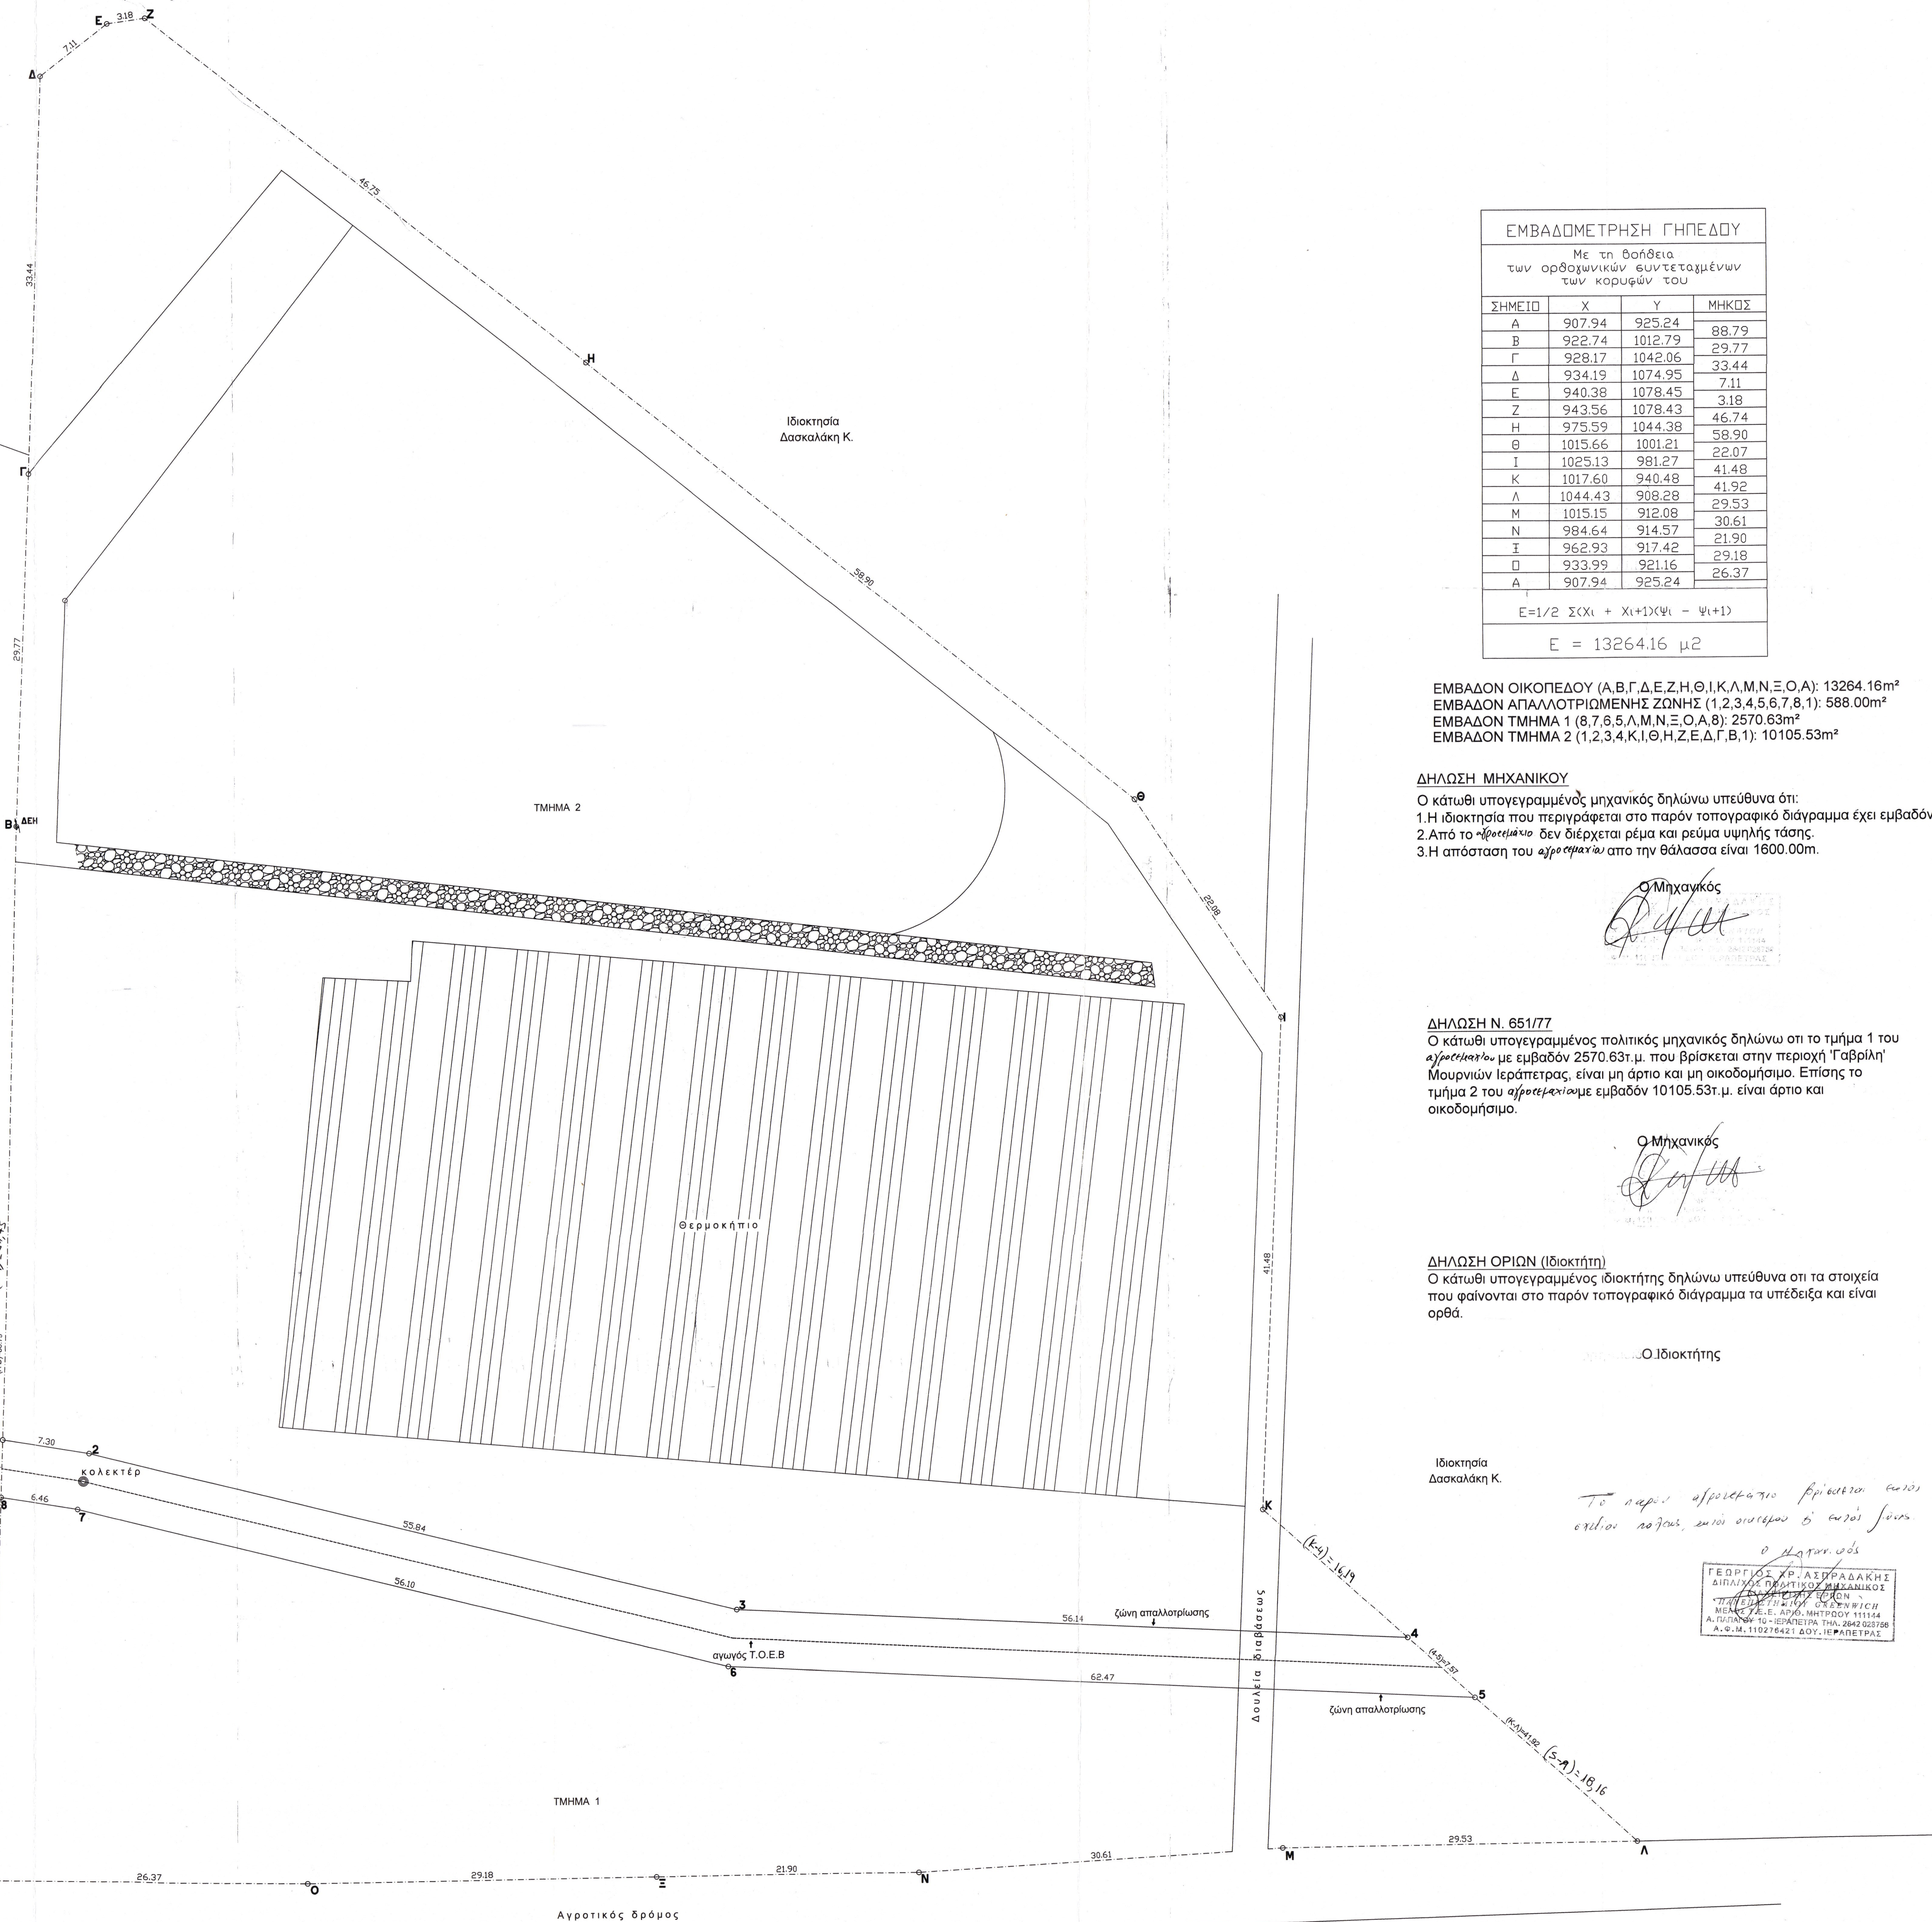




ΕΜΒΑΔΟΜΕΤΡΗΣΗ ΓΗΠΕΔΟΥ			
Με τη βοήθεια των ορθογωνικών συντεταγμένων των κορυφών του			
ΣΗΜΕΙΟ	X	Y	ΜΗΚΟΣ
A	907.94	925.24	88.79
B	922.74	1012.79	29.77
Γ	928.17	1042.06	33.44
Δ	934.19	1074.95	7.11
Ε	940.38	1078.45	3.18
Ζ	943.56	1078.43	46.74
Η	975.59	1044.38	58.90
Θ	1015.66	1001.21	22.07
Ι	1025.13	981.27	41.48
Κ	1017.60	940.48	41.92
Λ	1044.43	908.28	29.53
Μ	1015.15	912.08	30.61
Ν	984.64	914.57	21.90
Ξ	962.93	917.42	29.18
Ο	933.99	921.16	26.37
Α	907.94	925.24	
$E=1/2 \sum (X_i + X_{i+1})Y_i - Y_{i+1}$			
E = 13264.16 μ2			

ΕΜΒΑΔΟΝ ΟΙΚΟΠΕΔΟΥ (Α,Β,Γ,Δ,Ε,Ζ,Η,Θ,Ι,Κ,Λ,Μ,Ν,Ξ,Ο,Α): 13264.16m²
ΕΜΒΑΔΟΝ ΑΠΑΛΛΟΤΡΙΩΜΕΝΗΣ ΖΩΝΗΣ (1,2,3,4,5,6,7,8,1): 588.00m²
ΕΜΒΑΔΟΝ ΤΜΗΜΑ 1 (8,7,6,5,Λ,Μ,Ν,Ξ,Ο,Α,8): 2570.63m²
ΕΜΒΑΔΟΝ ΤΜΗΜΑ 2 (1,2,3,4,Κ,Ι,Θ,Η,Ζ,Ε,Δ,Γ,Β,1): 10105.53m²

ΔΗΛΩΣΗ ΜΗΧΑΝΙΚΟΥ

- Ο κάτωθι υπογεγραμμένος μηχανικός δηλώνω υπεύθυνα ότι:
- Η ιδιοκτησία που περιγράφεται στο παρόν τοπογραφικό διάγραμμα έχει εμβαδόν $E = 13264.16 \text{ m}^2$
 - Από το «*αφαιρούμενο*» δεν διέρχεται ρέμα και ρεύμα υψηλής τάσης.
 - Η απόσταση του *αφαιρούμενου* από την θάλασσα είναι 1600.00m.

Ο Μηχανικός
Γαβρής

ΔΗΛΩΣΗ Ν. 651/77

Ο κάτωθι υπογεγραμμένος πολιτικός μηχανικός δηλώνω ότι το τμήμα 1 του *αφαιρούμενου* με εμβαδόν 2570.63τ.μ. που βρίσκεται στην περιοχή 'Γαβρίλη' Μουρνιών Ιεράπετρας, είναι μη άρτιο και μη οικοδομήσιμο. Επίσης το τμήμα 2 του *αφαιρούμενου* με εμβαδόν 10105.53τ.μ. είναι άρτιο και οικοδομήσιμο.

Ο Μηχανικός
Γαβρής

ΔΗΛΩΣΗ ΟΡΙΩΝ (ιδιοκτήτη)

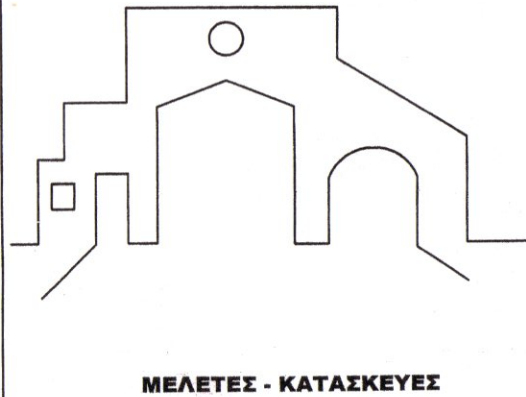
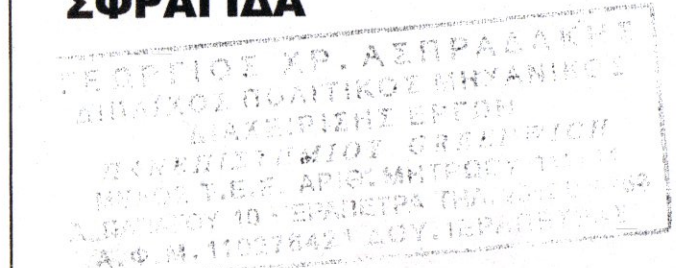
Ο κάτωθι υπογεγραμμένος ιδιοκτήτης δηλώνω υπεύθυνα ότι τα στοιχεία που φαίνονται στο παρόν τοπογραφικό διάγραμμα τα υπέδειξα και είναι ορθά.

Ο Ιδιοκτήτης

Ιδιοκτησία
Δασκαλάκη Κ.

Το παρόν *αφαιρούμενο* βρίσκεται πάνω
στην οδό, ενώ οι οικόπεδοι είναι
ο *αφαιρούμενος*

ΓΕΩΡΓΙΟΣ ΧΡ. ΑΣΠΡΑΔΑΚΗΣ
ΔΙΠΛΩΜΑΤΗΡΗΣ ΜΗΧΑΝΙΚΟΣ
ΠΟΛΙΤΙΚΟΣ ΜΗΧΑΝΙΚΟΣ
ΜΗΧΑΝ. Τ.Ε.Ε. ΑΡΧ. ΜΗΤΡΩΟΥ 11114
Α. ΠΛΑΤΕΙΑ 10 - ΙΕΡΑΠΕΤΡΑ ΤΗΛ. 0942 03708
Α.Φ.Μ. 110276421 ΔΟΥ. ΙΕΡΑΠΕΤΡΑΣ

 ΜΕΛΕΤΕ - ΚΑΤΑΣΚΕΥΕΣ		ΤΕΧΝΙΚΟ ΓΡΑΦΕΙΟ	
ΚΑΝΑΒΑΚΗΣ		ΘΕΟΔΟΣΗΣ	
ΑΣΠΡΑΔΑΚΗΣ		ΧΡΗΣΤΟΣ	
		Πολιτικός Μηχανικός Ε.Μ.Π.	
		Πολιτικός Μηχανικός Τ.Ε.	
ΕΡΓΟΔΟΤΗΣ		ΣΚΛΑΒΑΚΗΣ ΜΙΧΑΛΗΣ	
ΕΡΓΟ			
ΘΕΣΗ		"ΓΑΒΡΙΛΗ" ΜΟΥΡΝΙΩΝ ΙΕΡΑΠΕΤΡΑΣ	
ΘΕΜΑ		ΤΟΠΟΓΡΑΦΙΚΟ ΔΙΑΓΡΑΜΜΑ	
		ΑΡ. ΣΧΕΔΙΟΥ	
ΚΑΙΜΑΚΕΣ		1/200	
ΧΡΟΝΟΣ ΜΕΛΕΤΗΣ		ΑΥΓΟΥΣΤΟΣ 2008	
ΣΦΡΑΓΙΔΑ		ΥΠΟΓΡΑΦΗ	
		<i>Γαβρής</i>	